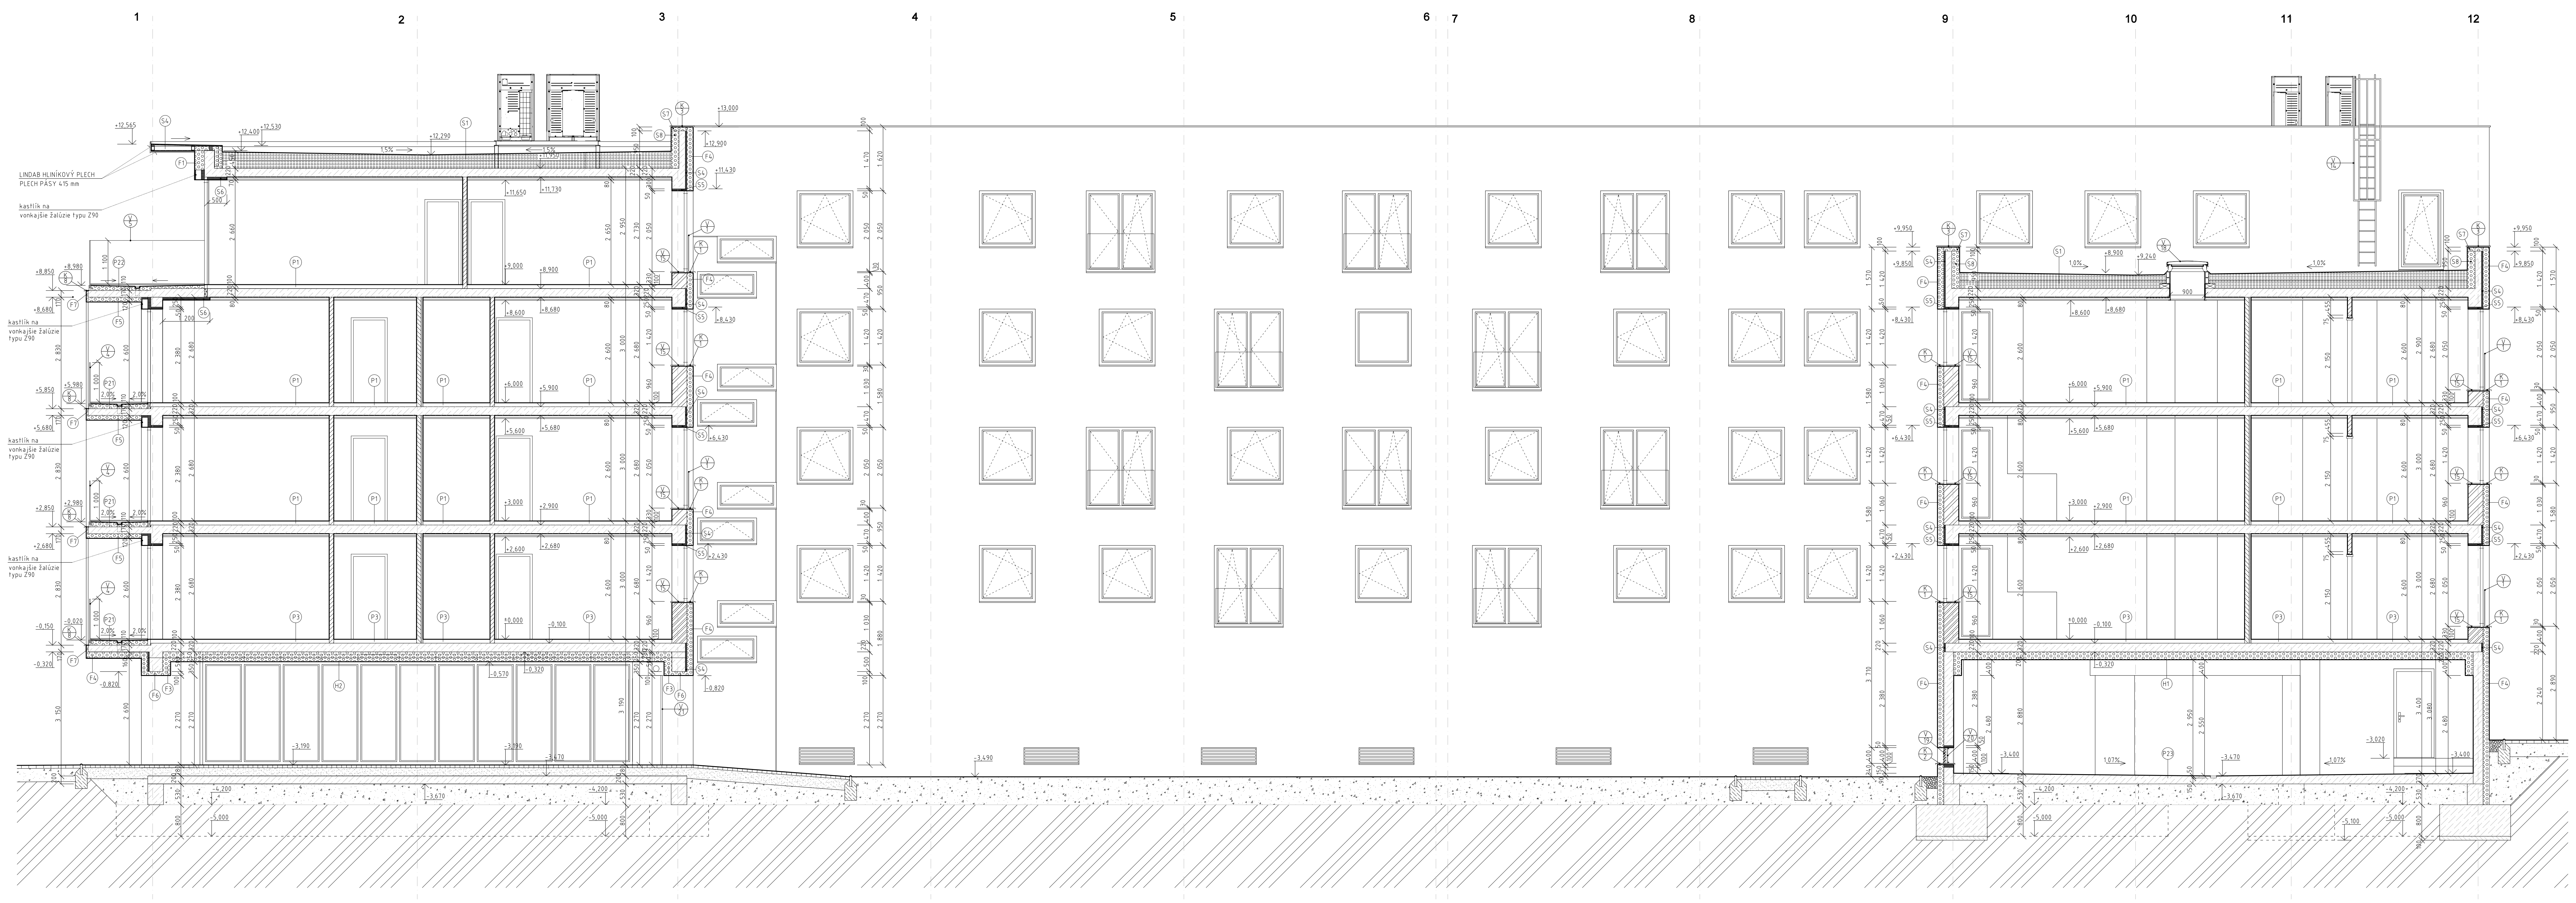

REZOPOHLAD C-C´ /medzi osami E-D/

SKLADBY KONŠTRUKCIÍ

(S1) STRECHA /ŠTRKOVÝ ZÁSYP/
- ŠTRKOVÝ ZÁSYP 100 mm
- GEOTEXTÍLIA
- FÓLIA FATRAFOL 810
- GEOTEXTÍLIA
- EXPANDOVANÝ POLYSTYRÉN EPS 150 S /AUSTROTHERM/ 340 – 510 mm
- PAROZÁBRANA
- ŽB stropná doska – 220 mm

(S2) STRECHA /RETENČNÁ/
- ROZCHODNÍKOVÁ ROHOŽ TopMat S/5 -30 mm
- EXTENZÍVNY SUBSTRÁT -60 mm
- HYBRIDNÁ DOSKA EnviBoard 20 – 20mm
- GEOTEXTÍLIA
- FÓLIA FATRAFOL 810
- GEOTEXTÍLIA
- EXPANDOVANÝ POLYSTYRÉN EPS 150 S /AUSTROTHERM/ 340 – 510 mm
- PAROZÁBRANA
- ŽB stropná doska – 220 mm

(S3) STRECHA /POCHôDZNA
- DLAŽBA NA PODLOŽKÁCH 20 mm
- FÓLIA FATRAFOL 810
- GEOTEXTÍLIA
- EXPANDOVANÝ POLYSTYRÉN EPS 150 S /AUSTROTHERM/ 340 – 510 mm
- PAROZÁBRANA
- ŽB stropná doska – 220 mm

(S4) STRECHA /RÍMSA/
- FÓLIA FATRAFOL 810
- GEOTEXTÍLIA
- QSB DOSKY 22 mm
- OCELOVÁ KONŠTRUKCIA
- QSB DOSKY 22 mm
- LINDAB HLINÍKOVÝ PLECH PÁSY 415 mm

(S4) ŽB PRVKY
- EXTRUDOVANÝ POLYSTYRÉN hr.40 mm

(S5) ŽB PRVKY
- EXTRUDOVANÝ POLYSTYRÉN hr.50 mm

(S6) ŽB PRVKY
- EXTRUDOVANÝ POLYSTYRÉN hr.70 mm

(S7) ŽB PRVKY
- EXTRUDOVANÝ POLYSTYRÉN hr.100 mm

(S8) ŽB PRVKY
- EXTRUDOVANÝ POLYSTYRÉN hr.200 mm

(S9) ŽB PRVKY
- EXTRUDOVANÝ POLYSTYRÉN hr.30 mm

(S10) STRECHA /VÝŤAH. ŠACHTA/
- FÓLIA FATRAFOL 810
- GEOTEXTÍLIA
- EXPANDOVANÝ POLYSTYRÉN EPS 150 S /AUSTROTHERM/ 220 –262,5 mm
- PAROZÁBRANA
- ŽB stropná doska – 200 mm

SB 1 DELIACE STENY LOGGIE
- hranol RHOMBUS 26x68 THERMOWOOD
- hranol 42x42xTRERMOWOOD
- fasádna fólia čierna TYVEK UV FACADE
- celopl. lepidlo aqapanel s výstužnou tkaninou
- aqapanel cement board – outdoor 12.5 mm
- konštrukcia aqapanel outdoor

SB 2 DELIACE STENY LOGGIE
- CERTIFIKOVANÝ FASÁDNY SYSTÉM /SILIKÁTOVÁ OMIETKA/
- penetrácia pod omietku
- celopl. lepidlo aqapanel s výstužnou tkaninou
- aqapanel cement board – outdoor 12.5 mm
- konštrukcia aqapanel outdoor

SB 3 DELIACE STENY LOGGIE
- CERTIFIKOVANÝ FASÁDNY SYSTÉM /SILIKÁTOVÁ OMIETKA/
- penetrácia pod omietku
- celopl. lepidlo aqapanel s výstužnou tkaninou
- min vlna 50 mm
- aqapanel cement board – outdoor 12.5 mm
- konštrukcia aqapanel outdoor

(H1) PODHLAD /GARÁŽE/
- ŽB stropná doska – 220 mm
- KAMENNÁ VLNA ROCKWOOL STROPROCK G – 200 mm

(H2) PODHLAD /PASÁŽ/
- ŽB stropná doska – 220 mm
- KAMENNÁ VLNA ROCKWOOL FRONTROCK L – 250 mm

(F1) FASÁDA
- CERTIFIKOVANÝ FASÁDNY SYSTÉM /SILIKÁTOVÁ OMIETKA/
- MINERÁLNA VLNA hr.250 mm spodné pásy EXTRUD. POLYST.
- MURIVO

(F2) FASÁDA
- CERTIFIKOVANÝ FASÁDNY SYSTÉM /SILIKÁTOVÁ OMIETKA/
- MINERÁLNA VLNA hr.240 mm spodné pásy EXTRUD. POLYST.
- MURIVO

(F3) FASÁDA
- CERTIFIKOVANÝ FASÁDNY SYSTÉM /SILIKÁTOVÁ OMIETKA/
- MINERÁLNA VLNA hr.200 mm spodné pásy EXTRUD. POLYST.
- MURIVO

(F4) FASÁDA
- CERTIFIKOVANÝ FASÁDNY SYSTÉM /SILIKÁTOVÁ OMIETKA/
- MINERÁLNA VLNA hr.160 mm spodné pásy EXTRUD. POLYST.
- MURIVO

(F5) FASÁDA
- CERTIFIKOVANÝ FASÁDNY SYSTÉM /SILIKÁTOVÁ OMIETKA/
- MINERÁLNA VLNA hr.120 mm spodné pásy EXTRUD. POLYST.
- MURIVO

(F6) FASÁDA
- CERTIFIKOVANÝ FASÁDNY SYSTÉM /SILIKÁTOVÁ OMIETKA/
- MINERÁLNA VLNA hr.100 mm spodné pásy EXTRUD. POLYST.
- MURIVO

(F7) FASÁDA
- CERTIFIKOVANÝ FASÁDNY SYSTÉM /SILIKÁTOVÁ OMIETKA/
- MINERÁLNA VLNA hr.50 mm spodné pásy EXTRUD. POLYST.
- MURIVO

(F8) FASÁDA
- CERTIFIKOVANÝ FASÁDNY SYSTÉM /SILIKÁTOVÁ OMIETKA/
- MINERÁLNA VLNA hr.40 mm spodné pásy EXTRUD. POLYST.
- MURIVO

AKCIA	BYTOVÝ DOM		
OBJEKT	SO-100 BYTOVÝ DOM		
INVESTOR	REALINVEST SK s.r.o., Tomášikova 23/E, BRATISLAVA		
MIESTO ST.	ŽIAR NAD HRONOM, p.č. 1149/68		
STUPEŇ	PROJEKT PRE STAVEBNÉ POVOLENIE		
ZODP.PROJ.	ING. LUBOSLAV PAVLA	DÁTUM	06/2022
MIERKA 1:50	OBSAH VÝKRESU REZOPOHLAD C-C´		v.č. 17