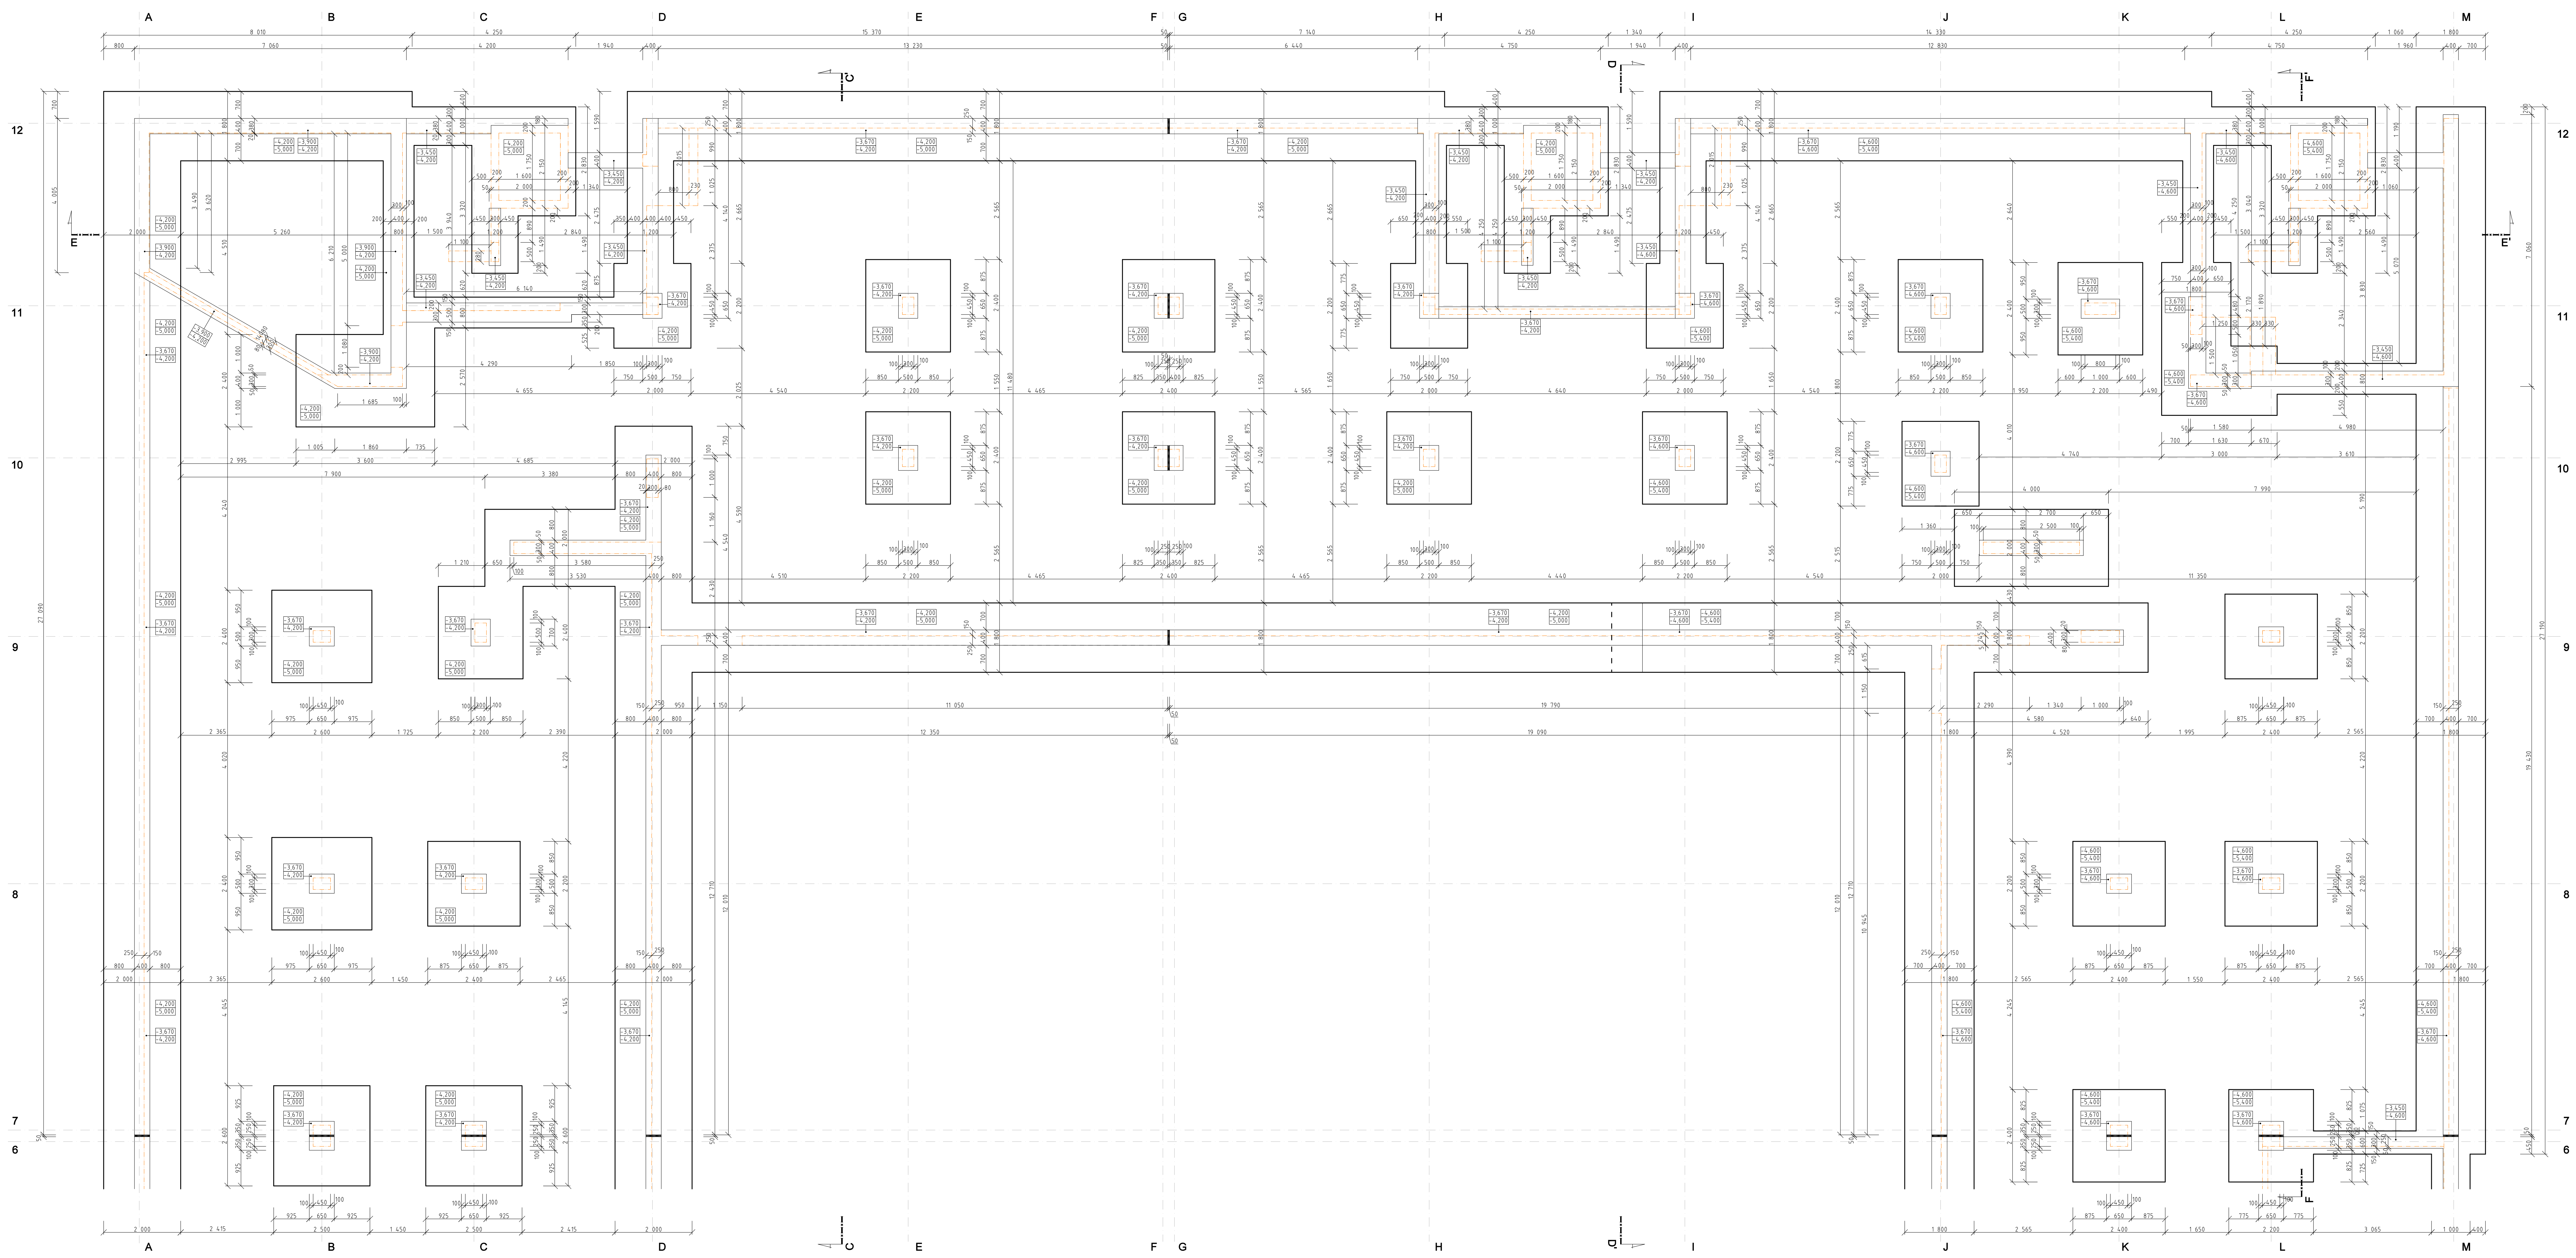

POZNÁMKA:

- SPODNÁ ÚROVEŇ ŽELEZOBETÓNOVÝCH PLOŠNÝCH ZÁKLADOV JE NAVRHOVANÁ V TROCH ÚROVNIACH /-5,1 m, -5,5 m a -5,9 m/ V PôDORYSE SÚ VÝŠKOVÉ KÓTY BEZ PODKLADNÝCH BETÓNOV /-5,0, -5,4 a -5,8 m/
- SPODNÁ ÚROVEŇ PLOŠNÝCH ZÁKLADOV JE NAVRHUTÁ Z PODKLADNÉHO BETÓNU TRIEDY C16/20 O HRÚBKE 100 mm
- V PRÍPADE ŽE V NAVRHOVANEJ HĹBKE NEBUDE DOSIAHNUTÁ VRSTVA ZEMINY G3/G-F JE NAVRHNUTÉ NAHRADENIE ZEMINY ZHUTNENOU ŠTRKOVOU VRSTVOU FRAKCIE 16 až 63 mm. MIERA ZHUTNENIA Edef=80,0 MPa. ŠTRKOVÝ NÁSYP JE NUTNÉ HUTNIŤ PO VRSTVÁCH O MAXIMÁLNEJ HRÚBKE 300 mm.
- POD PODKLADNÝ BETÓN AJ V PRÍPADOCH DOSIAHNUTÁ VRSTVY ZEMINY G3/G-F JE NAVRHNUTÉ JE NAVRHNUTÁ VRSTVA ZHUTNENÉHO ŠTRKU FRAKCIE 0 až16 mm V MINIMÁLNEJ HRÚBKE 100 mm. MIERA ZHUTNENIA Edef=80,0 MPa.
- VÝŠKA SPODNEJ ŽELEZOBETÓNOVEJ ČASTI PLOŠNÝCH ZÁKLADOV /PÁSY, PäTKY/ JE NAVRHNUTÁ 800 mm
- POD NOSNÝMI STENAMI A STĹPMI SÚ ŽELEZOBETÓNOVÉ ZÁKLADOVÉ KRČKY A TRÁMY
- ZÁKLADOVÉ TRÁMY BUDÚ V MIESTE SILATÁCII DILATOVANÉ
- POD ŽELEZOBETÓNOVÉ DOSKY PODLAHY PRÍZEMIA JE NAVRHNUTÁ VRSTVA ZHUTNENÉHO ŠTRKU FRAKCIE 16 až 63 mm - VÝŠKA PODĽA POTREBY, VRCHNÁ VRSTVA ZHUTNENÉHO ŠTRKU JE NAVRHOVANÁ FRAKCIE 0 až 16 mm V MINIMÁLNEJ HRÚBKE 100 mm. MIERA ZHUTNENIA ŠTRKOVEJ VRSTVY JE min. Edef= 40,0 MPa. ŠTRKOVÝ NÁSYP JE NUTNÉ HUTNIŤ PO VRSTVÁCH O MAXIMÁLNEJ HRÚBKE 300 mm.
- PO OBVODE OBJEKTU SÚ NAVRHNUTÉ SPäTNÉ ZÁSYPY 50% ZEMINA + 50% ŠTRK, HUTNIŤ PO VRSTVÁCH max. 300 mm NA MIERU ZHUTNENIA Edef= 20,0 MPa

ZÁKLADOVÉ PÁSY, KRČKY A TRÁMY : BETÓN C25/30 - XC3, XD1, XA1
VYSTUŽENÉ PRÚTMI BETONÁRSKEJ VÝSTUŽE
Z OCELE B500B A SIEŤOVINOU

ZÁKLADOVÉ DOSKY : BETÓN C30/37 - XC3, XD1, XF1, XA1- Cl 0,4 Dmax 22-S3
VYSTUŽENÉ PRÚTMI BETONÁRSKEJ VÝSTUŽE
Z OCELE B500B A SIEŤOVINOU

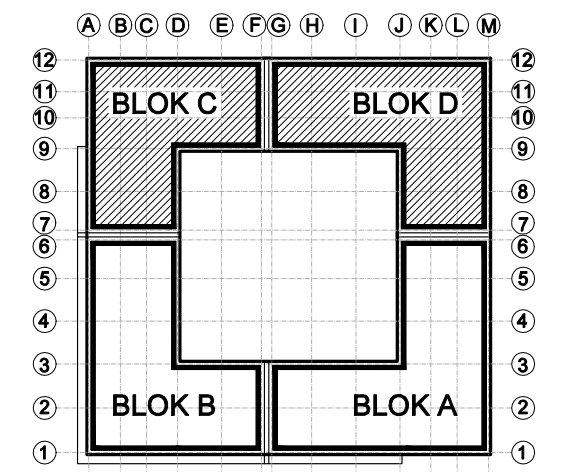

± 0,000=263,650

AKCIA	BYTOVÝ DOM		
OBJEKT	SO-100 BYTOVÝ DOM		
INVESTOR	REALINVEST SK s.r.o., Tomášikova 23/E, BRATISLAVA		
MIESTO ST.	ŽIAR NAD HRONOM, p.č. 1149/68		
STUPEŇ	PROJEKT PRE STAVEBNÉ POVOLENIE		
ZODP.PROJ.	ING. LUBOSLAV PAVLA	DÁTUM	05/2022
MIERKA 1:50	OBSAH VÝKRESU PôDORYS ZÁKLADOV - BLOK C,D		v.č. 2