


POHLAD Z JUHOVÝCHODU

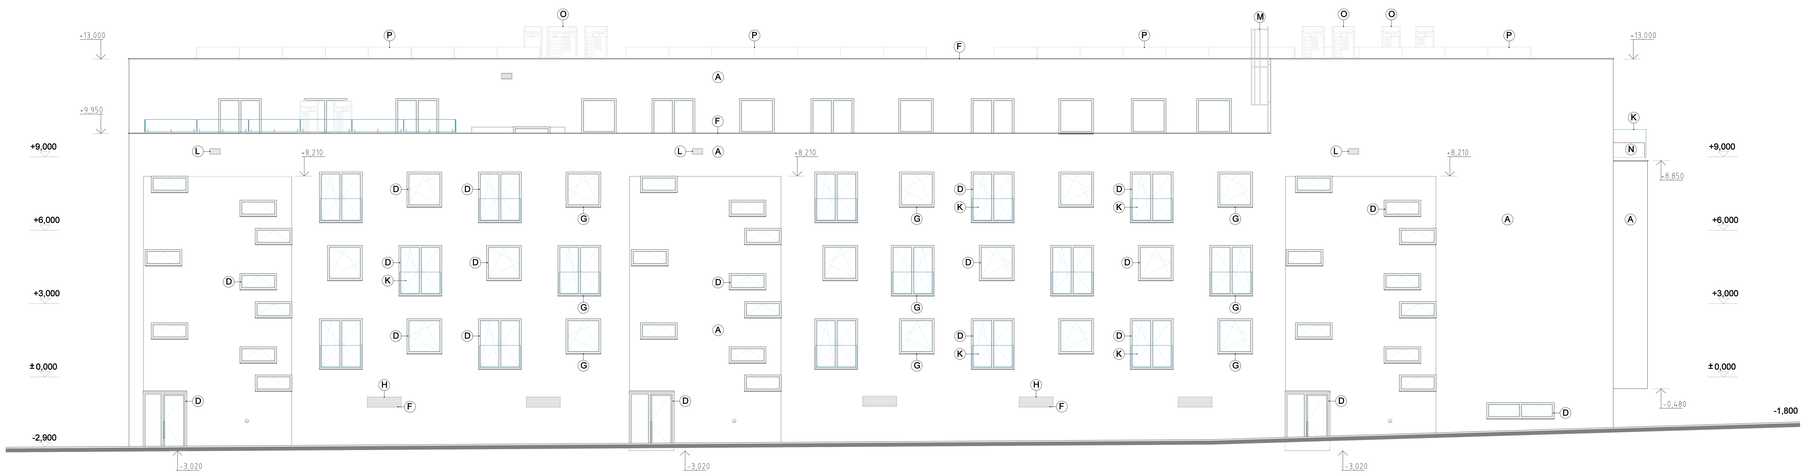

POHLAD OD SEVEROZÁPADU

LEGENDA POVRCHOVÝCH ÚPRAV

- (A) FASÁDA : FASÁDNA OMIETKA HLADENÁ, ZRNO 1,5 farba-BIELA BAUMIT LIFE 0019
- (B) RÍMSA : FALCOVANÝ HLINÍKOVÝ PLECH LINDAB farba- ANTRACITOVÁ RAL 7016
- (C) OBKLAD: hranol RHOMBUS 26x68 THERMOWOOD BOROVICA LESNÁ
- (D) OKNÁ, DVERE, PRESKLENÉ STENY: HLINÍK farba- ANTRACITOVÁ RAL 7016
- (E) GARÁŽOVÉ BRÁNY: OCELOVÝ PLECH farba-BLEDÁ SIVÁ MATNÁ
- (F) KLAMPIARSKE KONŠTR- HLINÍKOVÝ PLECH farba-BLEDÁ SIVÁ MATNÁ
- (G) KLAMPIARSKE KONŠTR- HLINÍKOVÝ PLECH farba- ANTRACITOVÁ RAL 7016
- (H) ŽALÚZIE : HLINÍKOVÝ PLECH farba-SIVÁ
- (I) ZÁMOCNÍCKE KONŠTR- OCEĽ ŽIAROVO POZINKOVANÁ + PRÁŠKOVANIE farba RAL 7016 matná
- (J) OSADZOVACÍ PROFIL SKLENENÝCH ZÁBRADLÍ : HLINÍKOVÝ PROFIL POVRCH. ÚPRAVA ACIER - AC
- (K) SKLENENÉ ZÁBRADLIA: KALENÉ LEPENÉ SKLO
- (L) VENTILAČNÉ MRIEŽKY: HLINÍK farba-BIELA
- (M) REBRÍK NA STRECHU: OCEĽ ŽIAROVO POZINKOVANÁ farba-SIVÁ
- (N) KVETINÁČ: BETÓN, alt.IMITÁCIA BETÓNU
- (O) STREŠNÉ JEDNOTKY DAIKIN: VÝROBOK
- (P) FOTOVOLTAICKÉ PANELY : VÝROBOK

AKCIA	BYTOVÝ DOM		
OBJEKT	SO-100 BYTOVÝ DOM		
INVESTOR	REALINVEST SK s.r.o., Tomášikova 23/E, BRATISLAVA		
MIESTO ST.	ŽIAR NAD HRONOM, p.č. 1149/68		
STUPEŇ	PROJEKT PRE STAVEBNÉ POVOLENIE		
ZODP.PROJ.	ING. LUBOSLAV PAVLA	DÁTUM	06/2022
MIERKA 1:100	OBSAH VÝKRESU POHLAD OD JV, SZ	v.č.	21