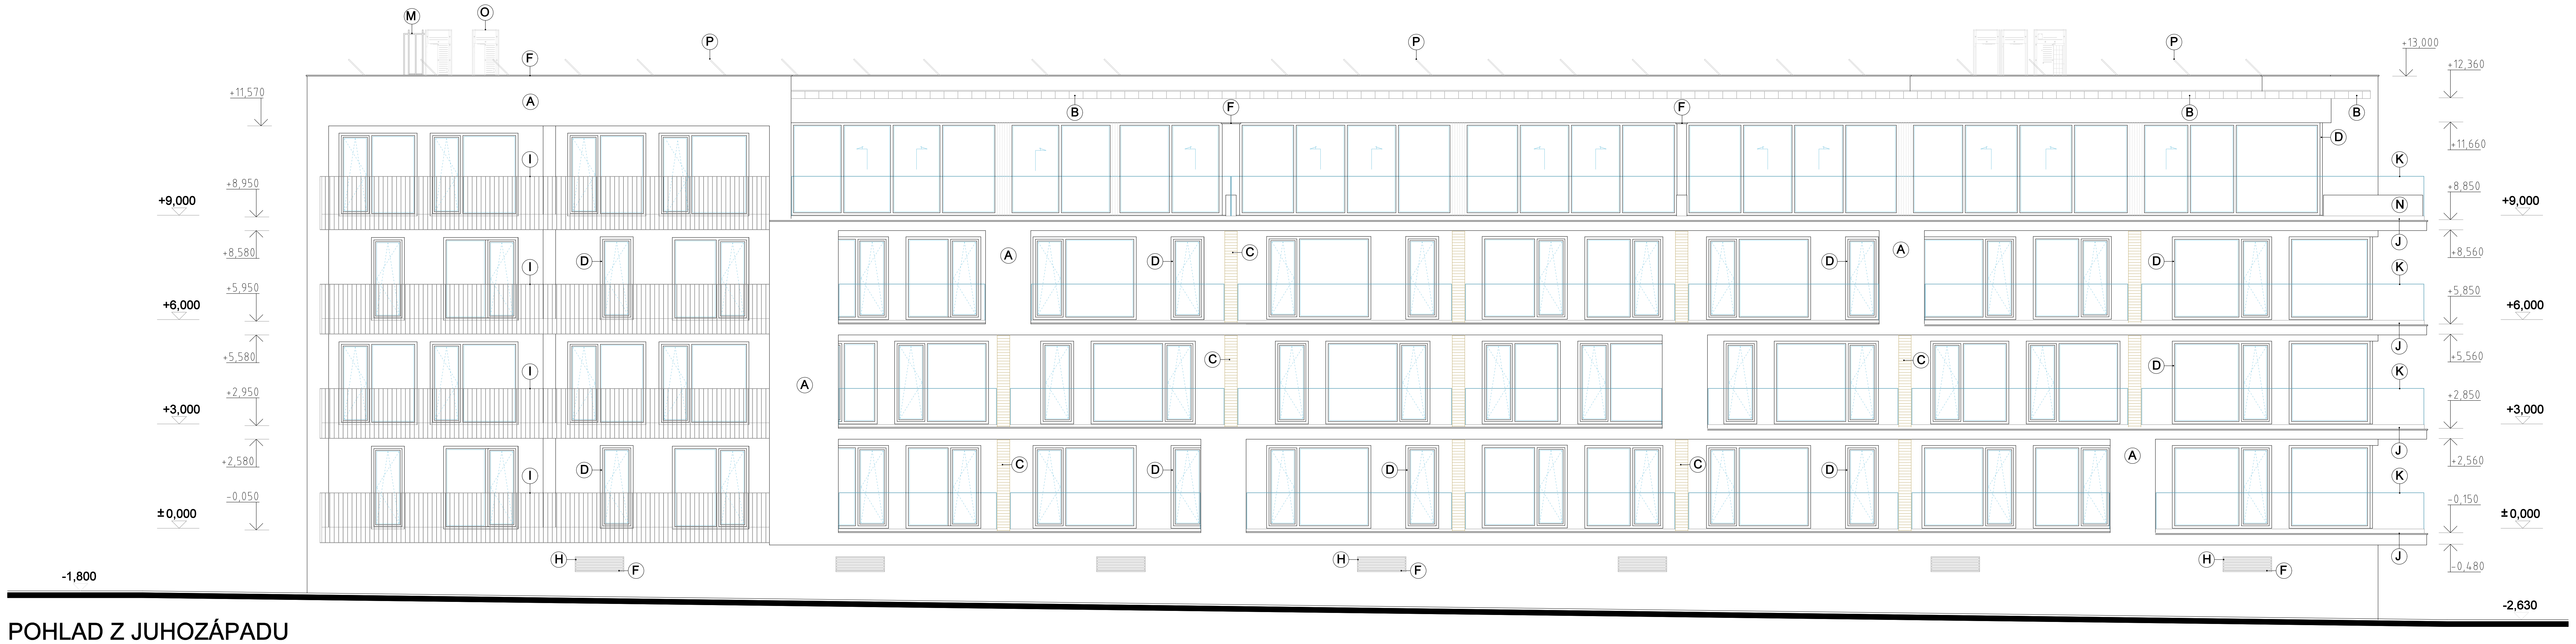

POHLAD Z JUHOZÁPADU

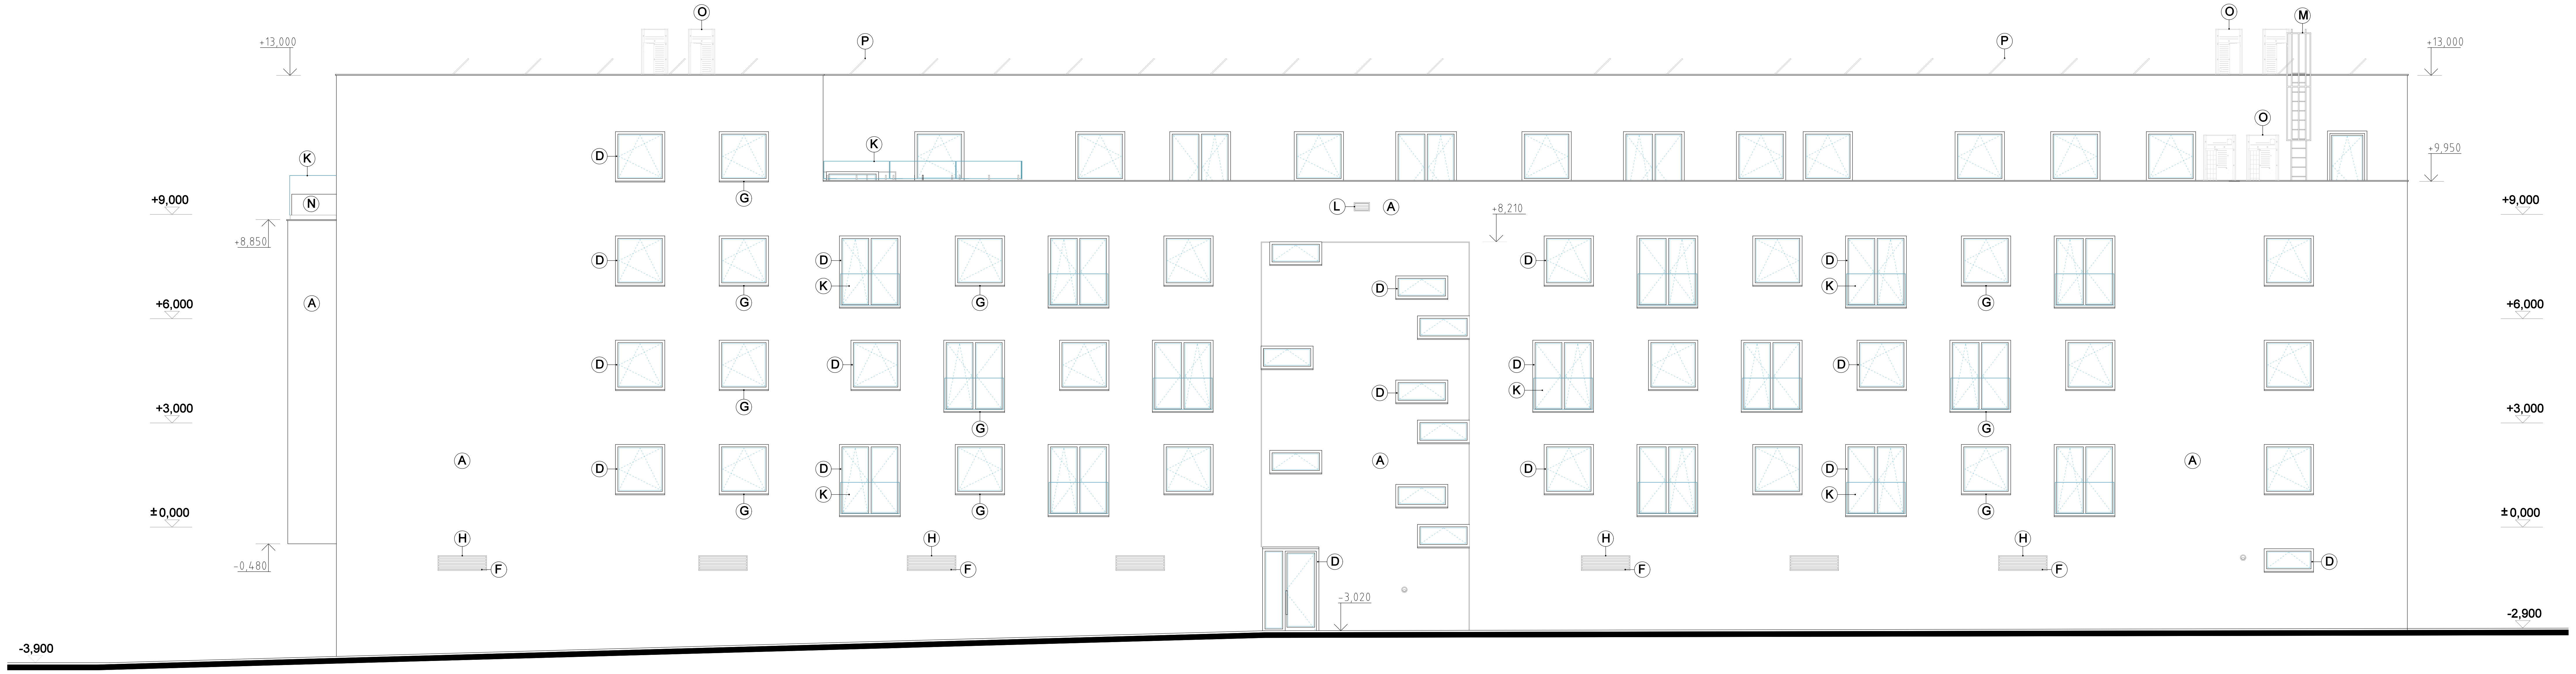

POHLAD OD SEVEROVÝCHODU

LEGENDA POVRCHOVÝCH ÚPRAV

Ⓐ	FASÁDA : FASÁDNA OMIETKA HLADENÁ, ZRNO 1,5 farba-BIELA BAUMIT LIFE 0019
Ⓑ	RÍMSA : FALCOVANÝ HLINÍKOVÝ PLECH LINDAB farba- ANTRACITOVÁ RAL 7016
Ⓒ	OBKLAD: hranol RHOMBUS 26x68 THERMOWOOD BOROVICA LESNÁ
Ⓓ	OKNÁ, DVERE, PRESKLENÉ STENY: HLINÍK farba- ANTRACITOVÁ RAL 7016
Ⓔ	GARÁŽOVÉ BRÁNY: OCELOVÝ PLECH farba-BLEDÁ SIVÁ MATNÁ
Ⓕ	KLAMPIARSKE KONšTR- HLINÍKOVÝ PLECH farba-BLEDÁ SIVÁ MATNÁ
Ⓖ	KLAMPIARSKE KONšTR- HLINÍKOVÝ PLECH farba- ANTRACITOVÁ RAL 7016
Ⓗ	ŽALÚZIE : HLINÍKOVÝ PLECH farba-SIVÁ
Ⓘ	ZÁMOCNÍCKE KONšTR- OCEL ŽIAROVO POZINKOVANÁ + PRÁŠKOVANIE farba RAL 7016 matná
Ⓙ	OSADZOVACÍ PROFIL SKLENENÝCH ZÁBRADLÍ : HLINÍKOVÝ PROFIL POVRCH. ÚPRAVA ACIER - AC
Ⓚ	SKLENENÉ ZÁBRADLIA: KALENÉ LEPENÉ SKLO
Ⓛ	VENTILAČNÉ MRIEŽKY: HLINÍK farba-BIELA
Ⓜ	REBRÍK NA STRECHU: OCEL ŽIAROVO POZINKOVANÁ farba-SIVÁ
Ⓝ	KVETINÁČ: BETÓN, alt.IMITÁCIA BETÓNU
Ⓞ	STREŠNÉ JEDNOTKY DAIKIN: VÝROBOK
Ⓟ	FOTOVOLTAICKÉ PANELY : VÝROBOK

AKCIA	BYTOVÝ DOM		
OBJEKT	SO-100 BYTOVÝ DOM		
INVESTOR	REALINVEST SK s.r.o., Tomášikova 23/E, BRATISLAVA		
MIESTO ST.	ŽIAR NAD HRONOM, p.č. 1149/68		
STUPEŇ	PROJEKT PRE STAVEBNÉ POVOLENIE		
ZODP.PROJ.	ING. LUBOSLAV PAVLA	DÁTUM	06/2022
MIERKA 1:100	OBSAH VÝKRESU POHLAD OD JZ, SV		v.č. 22